

بيانات خاصة بالموقع

الموقع	مخطط ولى العهد رقم ٣	
المنطقة	جنوب مكة الفرعية	
رقم القطعة	٥٦	رسم اللوحة الجوية
رقم الصك	٣٩٤٢٣٧...١٧٨	تاريخ الصك
مساحة الأرض بموجب الصك	٢م٦٢٥,٠٠	مساحة الأرض بموجب الطبيعة

حساب مسطحات البناء المسموحة

الشريحة الأرضية	مساحة الشريحة		أقصى ارتفاع مسموح للشريحة	١٣دوار
	أقصى نسبة بناء مسموحة في الشريحة	٪٦٥	معامل البناء	
	إجمالي مسطحات البناء المسموحة في الشريحة			
المنطقة الداخلية	مساحة الشريحة		أقصى ارتفاع مسموح للشريحة	
	أقصى نسبة بناء مسموحة في الشريحة		معامل البناء	
	إجمالي مسطحات البناء المسموحة في الشريحة			
المنطقة الخارجية	مساحة الشريحة		أقصى ارتفاع مسموح للشريحة	
	أقصى نسبة بناء مسموحة في الشريحة		معامل البناء	
	إجمالي مسطحات البناء المسموحة في الشريحة			
المساحات الخارجية	الاستقبال			
	المحفوظات			
	ترك مساحة من الأرض لصالح المالك			

حساب إجمالي مسطحات البروزات خارج المحدود

إجمالي البروزات	
-----------------	--

جدول مقدار البروز

بروز جنوبى		بروز غربى	
بروز شمالى		بروز شرقى	

البيانات الخاصة بمكونات الموقع

مكونات البناء	العدد	الوحدات	المساحة	النسبة المئوية	الاستخدام
الخزان الأرضى	١	١	٥٦,٧٦ م٢	—	خزان أرضى
الدور الأرضى	١	٥	١٥٥,٩٣ م٢	٪٦٣,٦٦	تجارى
		١	٢٤٢,٠٠ م٢		سكنى
دور الميزانين	١	١	٢٩٦,٦٠ م٢	٪٧٤,٥٣ من الأرضى	خدمات
بيت الدرج والمصاعد	١	١	٣٥,٧٥ م٢		درج ومصعد
الخزان العلوى	—	—	—	—	P. V. C
ال سور	١	١	٧٥,٠٠ م٢	—	سور
البيارة	١	١	٩,٠٠ م٢	—	بيارة صرف

حساب عدد المواقف المطلوب


المواقف المطلوبة	للسكنى	١ سيارات
	للتجارى	٩ سيارات
	للادارى	—
إجمالي عدد المواقف المطلوبة	١٠	النسبة
إجمالي عدد المواقف المتوفرة	١٠	

ملاحظة

البيانات والمسطحات أعلاه صحيحة وعلى مسئولية المكتب

التوقيع

الختم

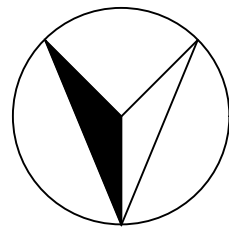

ملاحظة

يعتمد على مسئولية المكتب الهندسى ومتوافق مع كود البناء السعودى ومع الانظمة واللوائح المعتمدة التى تتطلبها وزارة النقل والادارة العامة للدفاع المدنى ووزارة المياه والكهرباء

دراسة	م.معمارى	نوع اللوحة ☐ معمارى ☐ انشائى ☐ كهرباء ☐ صحنى ☐ مخططات سلامة ☐ تكييف مركزى ☐ شبكات
ابتدائى	م.مراجع	
نهائى	م.انشائى	
رقم المشروع PROJ. No.	م.مراجع	
مقياس الرسم SCALE :	التاريخ DATE :	
1 / 100		

مكتب المهندس عمر بن سعيد بو سعيد للاستشارات الهندسية MAR BOSAEED CONSULTANT ENGINEER تصميم عمرانى تخطيط اشراف هندسى رفع مساحى دراسة الاحمال الكهربائية

مكة المكرمة الشوقية مبنى الانبار التجارى مقابل محطة الشوقية للمحروقات FAX-5335800 TEL-5335800 EMAIL-osboffice@hotmail.com


الموضوع SUBJECT :	المالك CLIENT :	رقم اللوحة
انشاء عمارة سكنية	على عبدالله ال سليمة القرنى	
عنوان اللوحة TITLE :	الموقع LOCATION :	
لوحة الجداول والمسطحات	مخطط ولى العهد رقم ٣	
01		SHEET NO.

منطقة جبلية

25.00

قطعة رقم ٨٥
ارض فضلاء

25.00

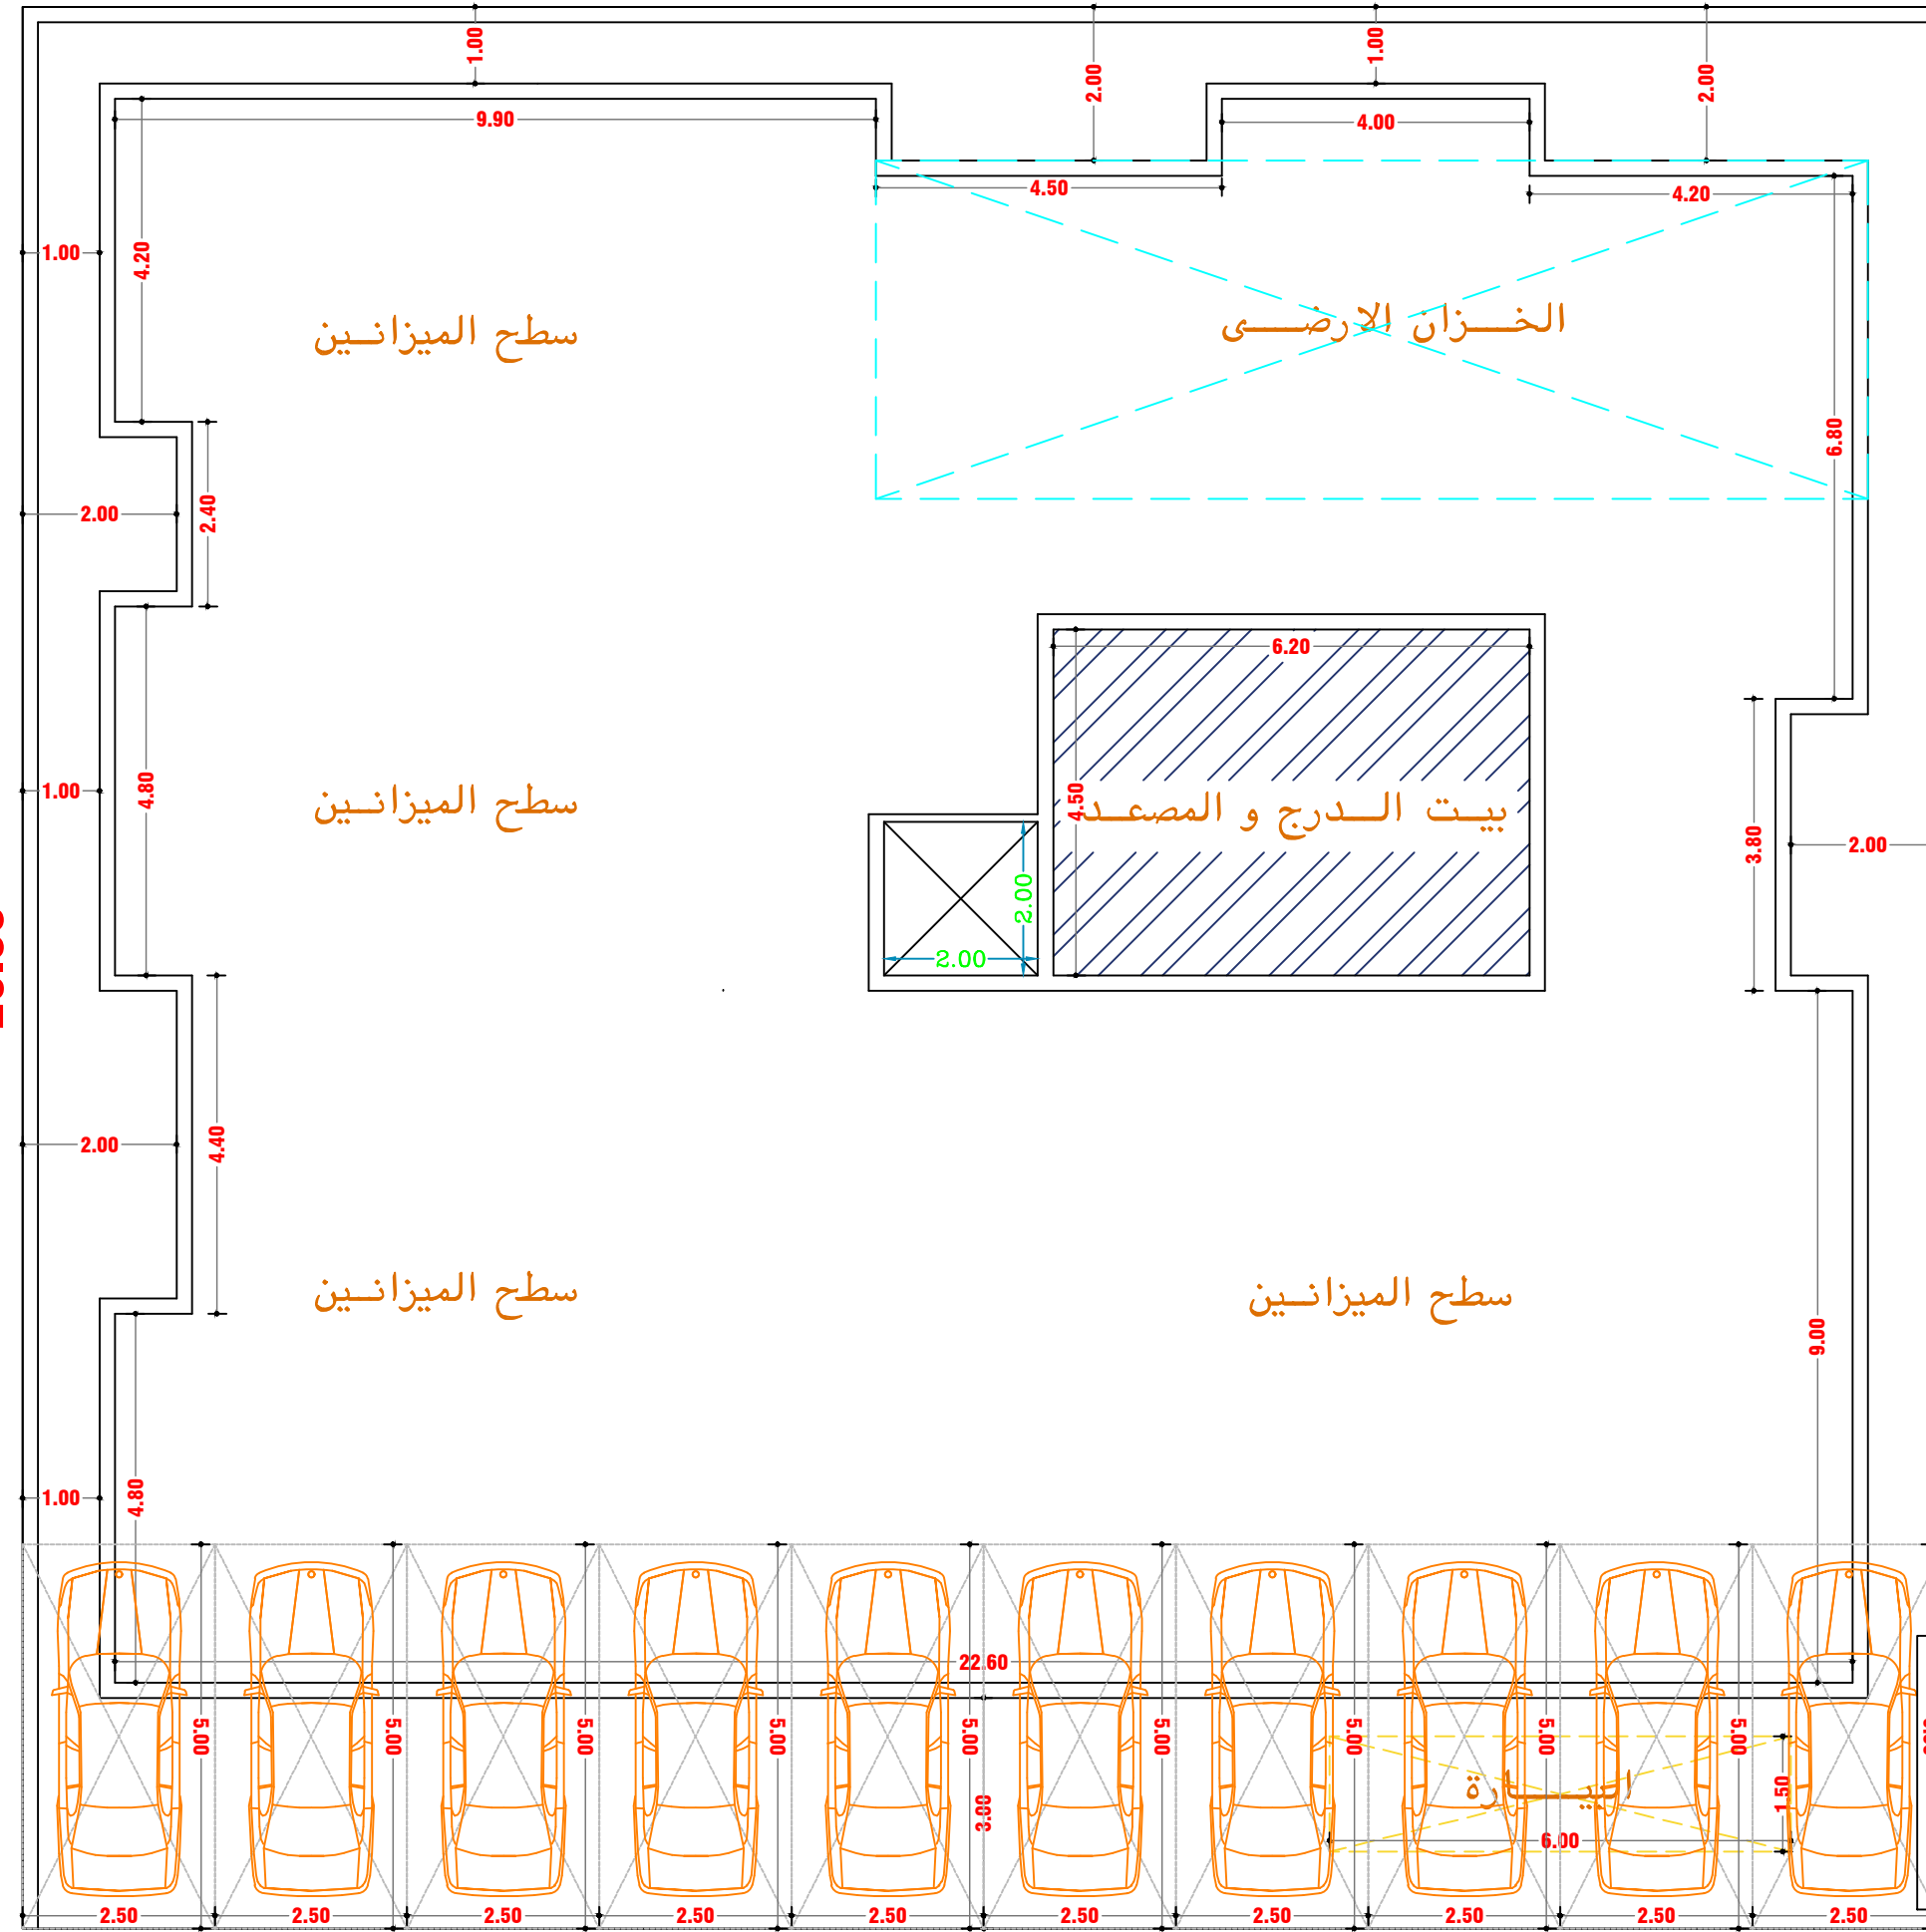

25.00

قطعة رقم ٥٥
ارض فضلاء

موقع العداد

25.00

شارع عرض ٥٢,٠٠ متر

ملاحظة

يعتمد على مسئولية المكتب الهندسى ومتوافق مع كود البناء السعودى ومع الانظمة واللوائح المعتمدة التى تتطلبها وزارة النقل والادارة العامة للدفاع المدنى ووزارة المياه والكهرباء

دراسة	م.معماري	نوع اللوحة
ابتدائي	م.مراجع	معماري
نهائي	م.انشائي	انشائي
رقم المشروع PROJ. No.	م.انشائي	كهرباء
مقياس الرسم SCALE :	م.مراجع	صحي
1 / 100	التاريخ DATE :	مخططات سلامة
		تكييف مركزي
		شبكات


مكتب المهندس عمر بن سعيد بو سعيد
للاستشارات الهندسية
MAR BOSAEED
CONSULTANT ENGINEER
تصميم عمراني تخطيط اشراف هندسي
رفع مساحي دراسة الاحمال الكهربائية

مكة المكرمة الشوقية
مبنى الانبار التجارى
مقابل محطة الشوقية للمحروقات
FAX-5335800 TEL-5335800
EMAIL-osboffice@hotmail.com

المالك CLIENT :	الموضوع SUBJECT :	رقم اللوحة
على عبدالله ال سليمة القرني	انشاء عمارة سكنية	
الموقع LOCATION :	عنوان اللوحة TITLE :	02
مخطط ولى العهد رقم ٣	الموقع العام	SHEET NO.

منطقة جبليّة

25.00

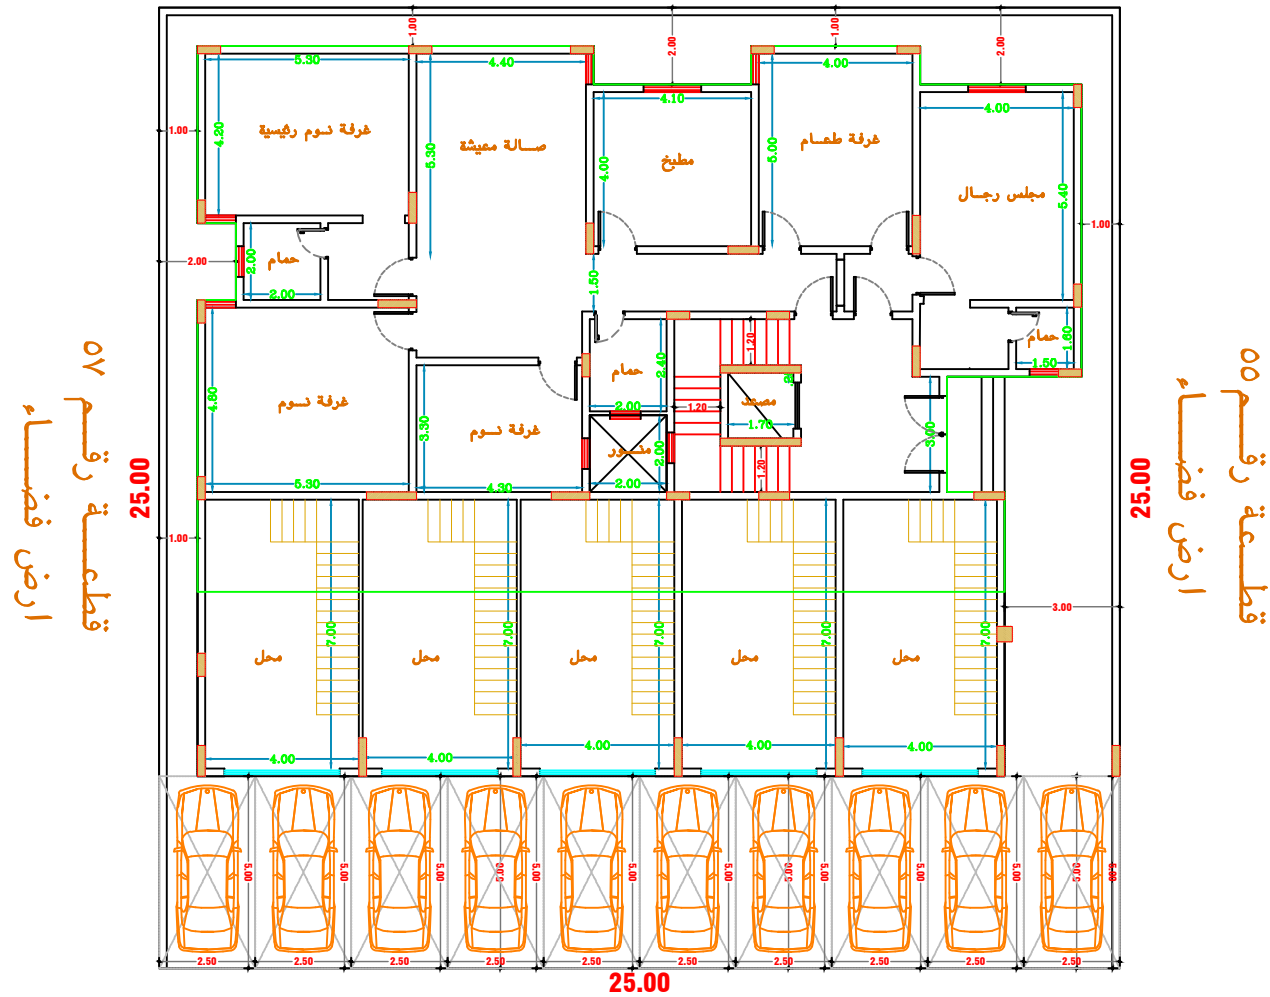

شارع عرض ۵۲,۰۰ متر

ملاحظة

يعتمد على مسؤولية المكتب الهندسي ومتوافق مع كود البناء السعودي ومع الانظمة واللوائح المعمدة التي تتطلبها وزارة النقل والادارة العامة للدفاع المدني ووزارة المياه والكهرباء

رقم اللوحة	الموضوع	الملك	CLIENT :
03	انشاء عمارة سكنية	علي عبدالله ال سليمة القرنى	
SHEET NO	عنوان اللوحة	الويع	LOCATION :
	مسقط افقى لدور الارضى	مخطط ولى المعد رقم ٣	

مكة المكرمة الشوقية	مكتب المهندس عمر بن سعيد بن سعيد
مبنى الانبار التجارى	للاستشارات الهندسية
مقابل محطة الشوقية للمحروقات	OMAR BOSAEED
	CONSULTANT ENGINEER
	تصميم عمرانى تخطيط اشراف هندسى
	رفع مساحى دراسة الاحمال الكهربائية

FAX-5335800	TEL-5335800
EMAIL-osboffice@hotmail.com	


نوع اللوحة	مسمار
مسمار	م
انشائي	م
كهروم	م
مخمس	م
مخططات سلامة	م
تخطيط مركزي	م
شبكة	م

PROJ. No.	رقم المشروع
SCALE :	مقياس الرسم
1 / 100	

DATE :	التاريخ
--------	---------

منطقة جبالية

25.00

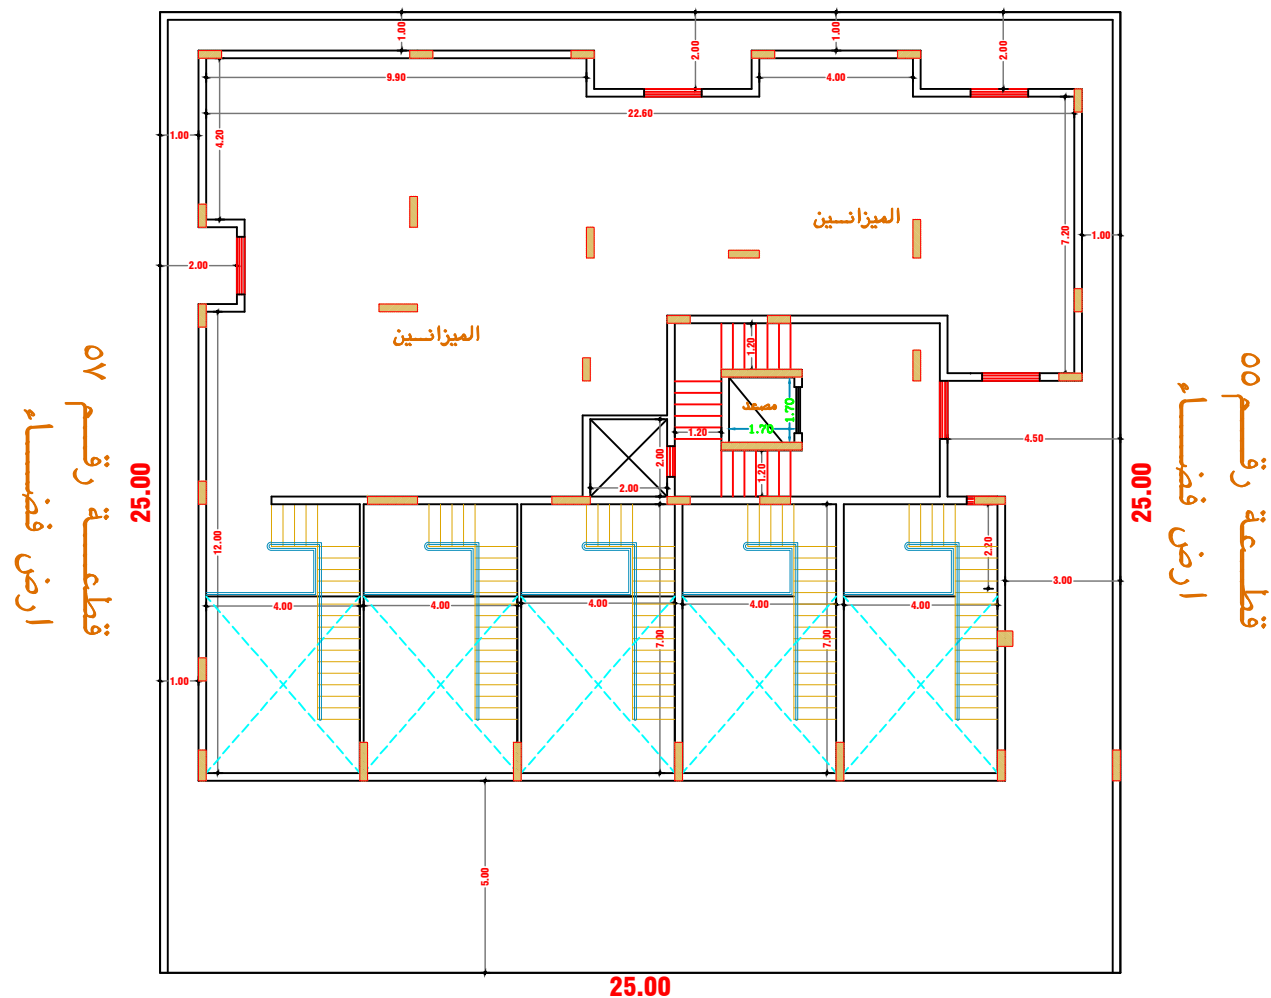

شارع عرض ٥٢,٠٠ متر

ملاحظة 🍊

يعتمد على مسغولية المكتب الهندسى وموافق
مع كود البناء السعودى ومع الانظمة واللوائح
المعتمدة التى تتطلبها وزارة النقل والادارة
العامة للدفاع المدنى ووزارة المياه والكهرباء


رقم اللوحة	الموضوع	التمالك	CLIENT :
04	انشاء عمارة سكنية	على عبدالله ال سليعة القرني	
SHEET NO	عنوان اللوحة	الموقع	LOCATION :
	مسقط افقى لدور الميزانين	مخطط ولى العهد رقم ٣	

م.معماري	نوع اللوحة	مكتب المهندس عمر بن سعيد بو سعيد
٢.مراجع	☐ معماری	للاستشارات الهندسية
٣.م.انشاء	☐ انشائي	OMAR BOSAEED
٤.مراجع	☐ كهربة	CONSULTANT ENGINEER
	☐ حصى	تصميم عمراني تخطيط اشراف هندسي
	☐ مخططات ساحة	رفع مساحي دراسة الاحمال الكهربائية
	☐ تكييف مركزي	
	☐ شبكات	

المقياس الرسم :	التاريخ	DATE :
1 / 100		

PROJ. No.	رقم المشروع
SCALE :	مقياس الرسم :
1 / 100	

مكة المكرمة الشوقية	مكة المكرمة الشوقية
مبنى الانبار التجاري	مبنى الانبار التجاري
مقابل محطة الشوقة للمحروقات	مقابل محطة الشوقة للمحروقات
FAX-5335800 TEL-5335800	FAX-5335800 TEL-5335800
EMAIL-osboffice@hotmail.com	EMAIL-osboffice@hotmail.com

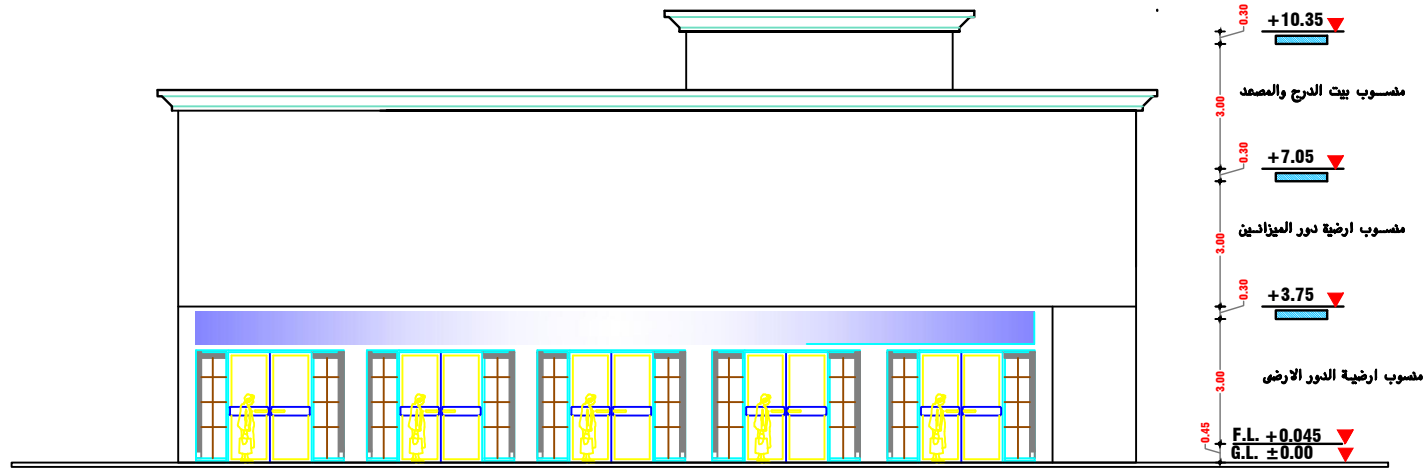

ملاحظة

يعتمد على مسغولية المكتب الهندسى ومتوافق مع كود البناء السعودى ومع الانظمة واللوائح المعمدة التى تتطلبها وزارة النقل والادارة العامة للدفاع المدنى ووزارة المياه والكهرباء

دراسة	م.م.م.م.	نوع اللوحة
استدلال	م.م.م.م.	م.م.م.م.
نموذج	م.م.م.م.	م.م.م.م.
PROJ. No.	م.م.م.م.	م.م.م.م.
SCALE : 1 / 100	DATE :	التاريخ

مكتب المهندس عمر بن سعيد بو سعيد
للاستشارات الهندسية
OMAR BOSAEED
CONSULTANT ENGINEER
تصميم عمرانى تخطيط اشراف هندسى
رفع مساحى دراسة الاحمال الكهربائية

مكة المكرمة الشوقية
مبنى الانبار التجارى
مقابل محطة الشوقية للمحروقات
FAX-5335800 TEL-5335800
EMAIL-osboffice@hotmail.com

CLIENT :	المالك /	SUBJECT :	الموضوع
LOCATION :	التوقع	TITLE :	عنوان اللوحة
مخطط ولى المعد رقم 3		الواجهة الرئيسية	

رقم اللوحة
05
SHEET NO.



رقم اللوحة	المالك /	الموضوع	SUBJECT :
06	علي عبدالله آل سليعة القرني	انشاء عمارة سكنية	انشاء عمارة سكنية
1 / 100	التوقيع	الموقع	عنوان اللوحة
1 / 100	التاريخ	مخططولى المعد رقم 3	القطاع


مكتب المهندس عمر بن سعيد بو سعيد للاستشارات الهندسية OMAR BOSAEED CONSULTANT ENGINEER تصميم عمراني تخطيط اشرف هندسي رفع مساحي دراسة الاحمال الكهربائية

مكة المكرمة الشوقية مبنى الانبار التجاري مقابل محطة الشوقية للمحروقات FAX-5335800 TEL-5335800 EMAIL-osboffice@hotmail.com

CLIENT :	المالك /	SUBJECT :	الموضوع
علي عبدالله آل سليعة القرني		انشاء عمارة سكنية	
LOCATION :	التوقيع	TITLE :	عنوان اللوحة
مخططولى المعد رقم 3		القطاع	

جدول نماذج الاعمدة


رقم	الدور الارضى		الدور المتكرر		المبنيات	
	قطاع	تسليح	قطاع	تسليح	قطاع	تسليح
١ ع	٦.٠×٢.٠	١٦ Ø ٨	٦.٠×٢.٠	١٦ Ø ٨	٦.٠×٢.٠	١٦ Ø ٨
٢ ع	٨.٠×٢.٠	١٦ Ø ١٠	٨.٠×٢.٠	١٦ Ø ١٠	٨.٠×٢.٠	١٦ Ø ١٠
٣ ع	١٠.٠×٢.٠	١٦ Ø ١٢	١٠.٠×٢.٠	١٦ Ø ١٢	١٠.٠×٢.٠	١٦ Ø ١٢
٤ ع	١٢.٠×٢.٠	١٦ Ø ١٦	١٢.٠×٢.٠	١٦ Ø ١٦	١٢.٠×٢.٠	١٦ Ø ١٦
٤ ع	٤.٠×٤.٠	١٦ Ø ١٠				
ح	كما بالشكل ١٤/٦ م					
كانات	٨/٦ م		٨/٦ م		٨/٦ م	

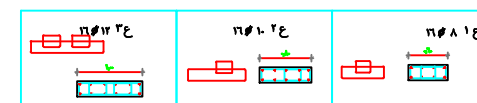

ملاحظات الاعمدة

- × صممت الاعمدة على اساس ان المبنى مكون من الادوار الاتية خمسة ادوار
- × اجهاد الكسر لمكعبات الخرسانة القياسية لا يقل عن ٣٥٠ كج/سم^٣ وذلك بعد ٢٨ يوم من تاريخ الصب
- × الحديد المستخدم عالي المقاومة (٦٠/٤٠) اجهاد التشغيل ٢٠٠٠ كج/سم^٢ يجب استخدام اسمنت مقاوم في الاجزاء الخرسانية المدفونة
- × الخرسانة المسلحة مكونة من ٨٠-٣٠٠ كج/م^٣ متدرج + ٤٠-٣٠٠ رمل + ٣٥٠ كج/م^٣ اسمنت بورتلاند ونسبة المياه لا تتعدى ٤٥٪ من وزن الاسمنت
- × يجب معالجة الخرسانة بعد الصب وذلك برشها مرتين يوميا في غياب الشمس لمدة اسبوعين على الاقل
- × يجب تجنب التكسير في الاعمدة عند عمل الاعتاب وذلك بزراع اشاير للاعتاب قبل صب الاعمدة

- × يتم وضع كانات عيون بالاعمدة كل ١ م
- × يجب مراجعة التفاصيل الانشائية قبل التنفيذ
- × يجب مراجعة المحاور والابعاد مع اللوحات المعمارية قبل بدء التنفيذ
- × التصميم الانشائي مسؤولية المكتب والتنفيذ مسؤولية المقاول
- × الاعمدة التي تكون بالخزان يتم زيادة قطاعها ليصبح الغطاء الخرساني ٥ سم من كل وجه ملاصق للماء
- × يتم استخدام بسكوت مناسب للحصول على الغطاء الخرساني المطلوب
- × يجب الالتزام بارتفاع الاعمدة كما هو مطلوب والا يلتزم المقاول بازالة الاجزاء الزائدة قبل البدء في الاعمال التالية
- × يتم زوى حديد البرندات (حديد حائط الخزان الافقي) عند الاطراف

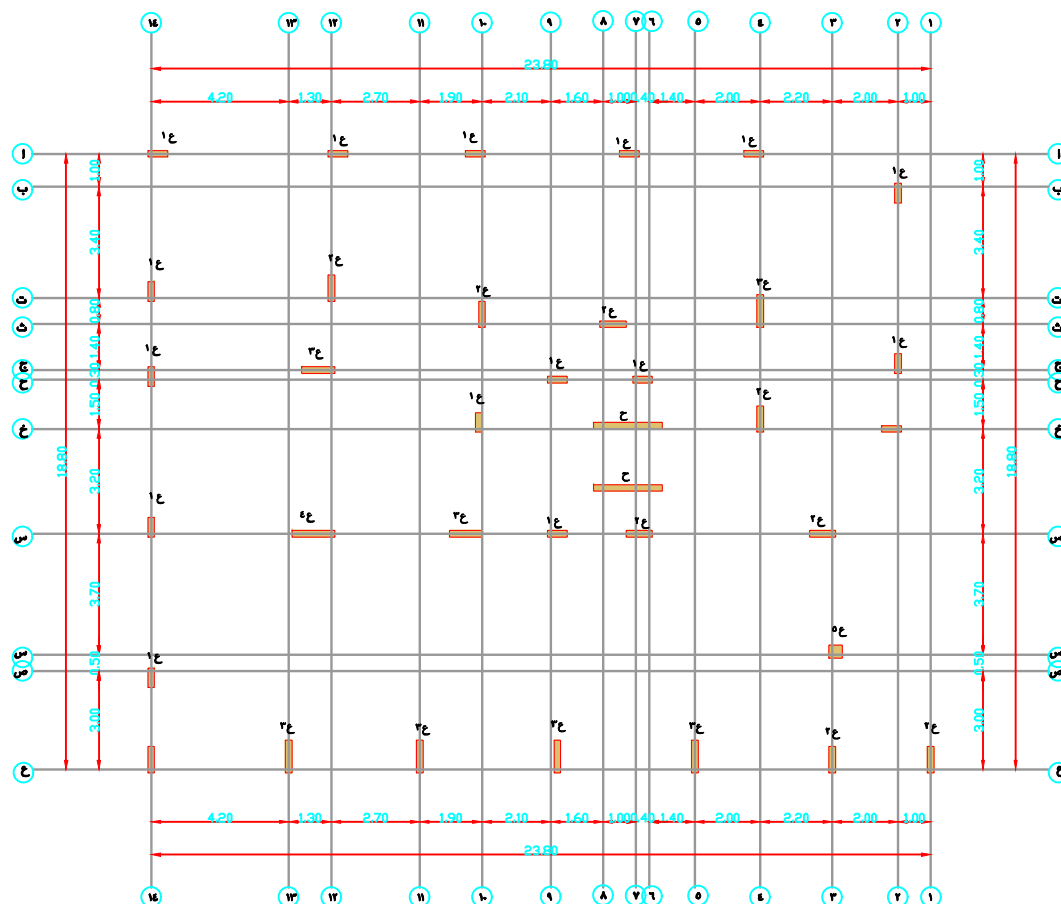

مكتب المهندس عمر بن سعيد
للاستشارات الهندسية
OMAR BOSAEED
CONSULTANT ENGINEER
تصميم عمارة تخطيط اشراف هندسي
رفع مساحي دراسة الاحمال الكهربائية

مكة المكرمة الشوكية
مبنى الانبار التجاري
مقابل محطة الشوكية للمحروقات
FAX-5335800 TEL-5335800
EMAIL-osboffice@hotmail.com

CLIENT : المالك

على عبدالله ال سليمة القرني

LOCATION : الموقع

مخطط ولى العهد رقم ٣

SUBJECT : الموضوع

انشاء عمارة سكنية

TITLE : عنوان اللوحة

الاعمدة

رقم اللوحة

01

SHEET NO

جدول القواعد


النموذج	خرسانة عادية		خرسانة مسلحة		التسليح السفلي		التسليح العلوي	
	طول	عرض	سمك	طول	عرض	سمك	عرض	سمك
ق ١	٢١٥	١٧٥	١٠	١٩٥	١٥٥	٦٠	١٦ # ١٦	١٦ # ١٦
ق ٢	٣٦٥	٢٠٥	١٠	٢٤٥	١٨٥	٦٠	١٦ # ١٧	١٦ # ١٦
ق ٣	٣٢٠	٢٤٠	١٠	٣٠٠	٢٢٠	٦٠	١٦ # ٢٠	١٦ # ١٦
ق ٤	٣٧٠	٢٧٠	١٠	٣٥٠	٢٥٠	٧٠	١٦ # ٢٥	١٦ # ١٦
ق م	كما بالشكل		كما بالشكل		٦ # ١٤ م/٨٤		٦ # ١٤ م/٨٤	٦ # ١٤ م/٨٤

جدول الشدادات

النموذج	العرض	الارتفاع	التسليح السفلي	التسليح	الكانات	ملاحظات
ش ١	٨٠	٦٠	٨ # ١٦	١٤ # ١٨	٦ م/١٢	٤ فروع

ملاحظات الاساسات

- صممت الاساسات على اساس ان المبنى مكون من الادوار الاتية دور أرضي + ٣ دور متكرر مبيتات
- اجهاد الكسر لمكعبات الخرسانة القياسية لا يقل عن ٣٠٠ كج/سم وذلك بعد ٢٨ يوم من تاريخ الصب
- الحديد المستخدم على المقاومة (٦٠/٤٠) اجهاد التشغيل ٤٠٠٠ كج/سم
- يجب استخدام اسمنت مقاوم في الاجزاء الخرسانية المدفونة
- الخرسانة المسلحة مكونة من ٠,٨٠ م ركام متدرج ٠,٤٠ م رمل + ٣٥٠ كج اسمنت بورتلاند
- يجب معالجة الخرسانة بعد الصب وذلك برشها مرتين يوميا في غياب الشمس
- يجب تجنب التكسير في الاعمدة عند عمل الاعتبار وذلك بزرع اشاير للاعتاب قبل صب الاعمدة
- لاتزيد المسافة بين افرع الكانات عن ٣٠ سم
- يجب مراجعة التفاصيل الانشائية قبل التنفيذ
- يجب مراجعة المحاور والابعاد مع اللوحات المعمارية قبل بدء التنفيذ
- صممت الاساسات على اساس ان قدرة تحمل التربة ٢ كجم/سم^٢

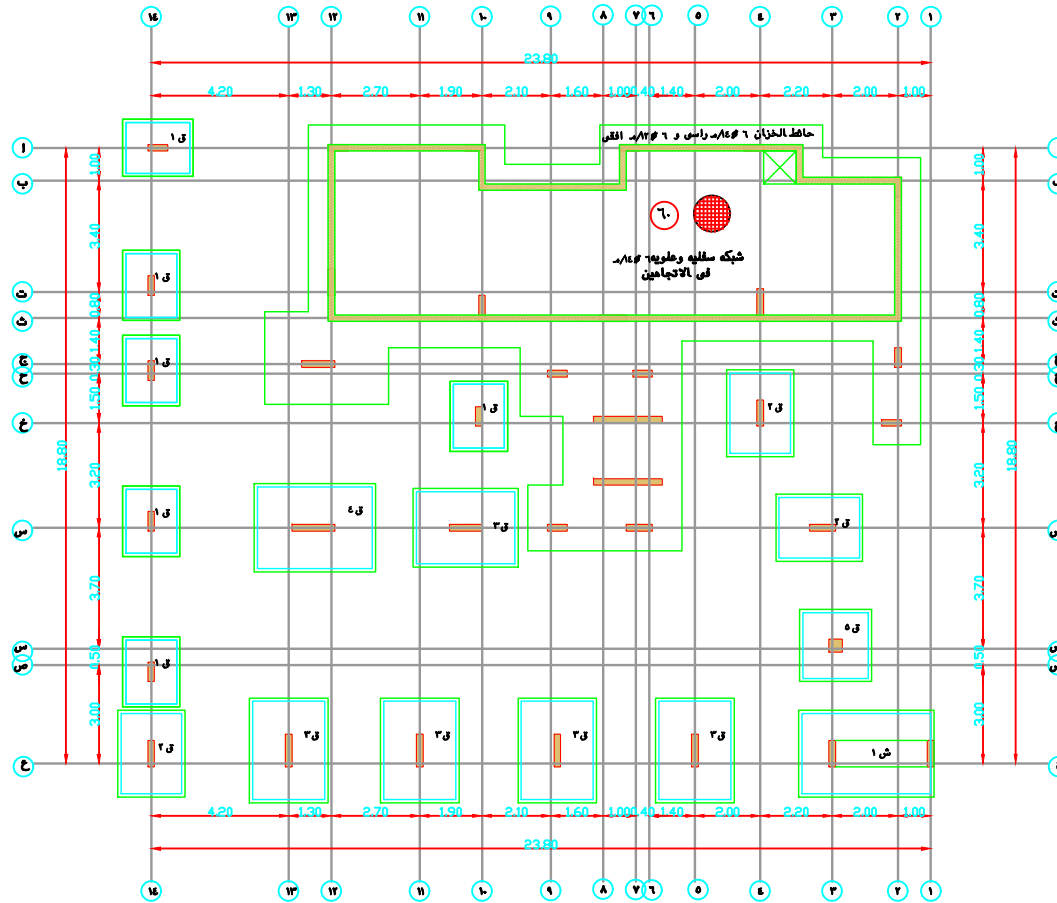

مكتب المهندس عمر بن سعيد بو سعيد
للاستشارات الهندسية
OMAR BOSAEED
CONSULTANT ENGINEER
تصميم عمارة تخطيط اشراف هندسي
رفع مساحي دراسة الاحمال الكهربائية

مكة المكرمة الشرقية
مبنى الانبار التجاري
مقابل محطة الشوكة للمحروقات
FAX-5335800 TEL-5335800
EMAIL-osboffice@hotmail.com

CLIENT : المالك

على عبدالله ال سليمة القرني

LOCATION : الموقع

مخطط ولي العهد رقم ٣

SUBJECT : الموضوع

انشاء عمارة سكنية

TITLE : عنوان اللوحة

الاساسات

رقم اللوحة

02


SHEET NO

جدول الميدات

النموذج	العرض	الارتفاع	التسليح السفلي	التسليح العلوي	الكانات	ملاحظات
١ م	٢٠	٦٠	١٦ Ø ٣	١٦ Ø ٣	٨/٨ م	
٢ م	٢٠	٦٠	١٤ Ø ٣	١٤ Ø ٣	٨/٨ م	
٣ م	٢٠	٦٠	١٦ Ø ٥	١٦ Ø ٣	٨/٨ م	

ملاحظات الميدات

- ١ - الميدات التي بجزءها أقل من ٣٠٠ سم يستبدل التسليح المكسح بحديد عدل
- ٢ - يتم تكسيح الميدات المستمرة عند ٥/١ البحر ويمتد الحديد العلوي إلى البحر المجاور
- ٣ - يتم التكميخ بزاوية ٤٥ والكمرات التي يزيد عمقها عن ٧٠ سم بزاوية ٦٠
- ٤ - يتم حزام الأعمدة بكافة عيون من أعلى أثناء الصب
- ٥ - يتم زوى الحديد العلوي عند النهايات الغير مستمرة
- ٦ - يتم خفض منسوب سطح الميدات بمقدار ١٠ سم عن سطح الخزان ما لم يذكر خلاف ذلك ويجب مراجعة المهندس المشرف قبل التنفيذ

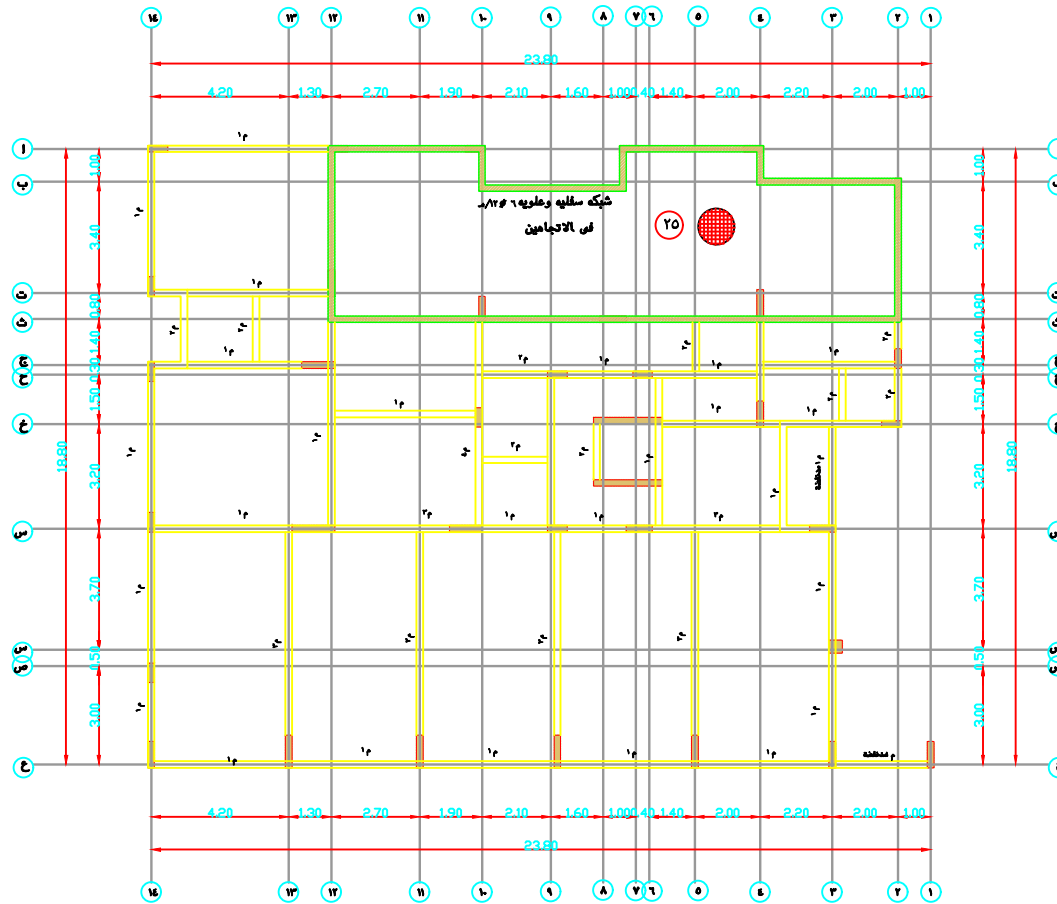

مكتب المهندس عمر بن سعيد بو سعيد
للاستشارات الهندسية
OMAR BOSAEED
CONSULTANT ENGINEER
تصميم عمارة تخطيط أشرف مهندس
رفع مساحي دراسة الاحمال الكهربائية

مكة المكرمة الشوكية
مبنى الانبار التجاري
مقابل محطة الشوكية للمحركات
FAX-5335800 TEL-5335800
EMAIL-osboffice@hotmail.com

CLIENT : المالك

على عبدالله ال سليمة القرني

LOCATION : الموقع

مخطط ولى العمد رقم ٣

SUBJECT : الموضوع

انشاء عمارة سكنية

TITLE : عنوان اللوحة

الميدات

رقم اللوحة

03

SHEET NO

جدول نماذج تسليح الكمرات

النموذج	التسليح السفلي		التسليح العلوي	الكانات	ملاحظات
	مكسح	عدل			
ك ١	١٦ # ٣	---	١٢ # ٣	٨ # ٥ م	
ك ٢	١٦ # ٤	---	١٤ # ٣	٨ # ٥ م	
ك ٣	١٦ # ٦	---	١٦ # ٣	٨ # ٥ م	
ك ٤	١٦ # ٦	---	١٦ # ٦	٨ # ٥ م	٤ فروع
ك ٥	١٨ # ٢٥	١٦ # ٨	١٨ # ١٢	٨ # ٢ م	٤ فروع
ك ٦	١٦ # ١٨	---	١٦ # ٦	٨ # ٢ م	٤ فروع
ك ١	١٦ # ٣	---	١٦ # ٣	٨ # ٥ م	
ك ٢	١٦ # ٣	---	١٦ # ٦	٨ # ٥ م	

ملاحظات الاسقف

× اجهاد كسر المكعبات القياسية $10 \times 10 \times 10$ سم للخرسانة المسلحة المستخدمة في صب الاسقف ٣٠٠ كجم سم وذلك بعد ٢٨ يوم من صبها والخطة المقترحة هي ٨٠م ٣م ٨٠م ٣م ٤٠م ٣م ٤٠م ٣٥٠ كجم اسمنت بورتلاند عادي ومحتوى المياه لا يتعدى ٤٥٪ من وزن الاسمنت يمتد حديد الكوابيل والشوك مرة ونصف طول البروز ويمتد الى الامام الحديد العلوي والمكسح والحديد يستمر الى نهاية الكابولي

النوعى عن ٨٠٠ كج / م



× ويمتد الحديد العلوي الى ١/٤ البحر المجاور الكمرات التي لا يوجد بها حديد مكسح يراعى مد تسليحها العلوي الى ١/٤ البحر المجاور

× يتم التكميش بزواوية ٤٥ والكمرات التي يزيد عمقها عن ٧٠ سم على زاوية ٦٠

× كانات الاعمدة داخل الكمرات والبلاطات يجب معالجة الخرسانة بعد الصب وذلك برشها مرتين يوميا في غياب الشمس

× يجب مراجعة التفاصيل الانشائية قبل التنفيذ

× يجب مراجعة المحاور و الأبعاد مع اللوحات المعمارية قبل بدء التصميم الانشائي مسؤولية المكتب والتنفيذ مسؤولية المقاول

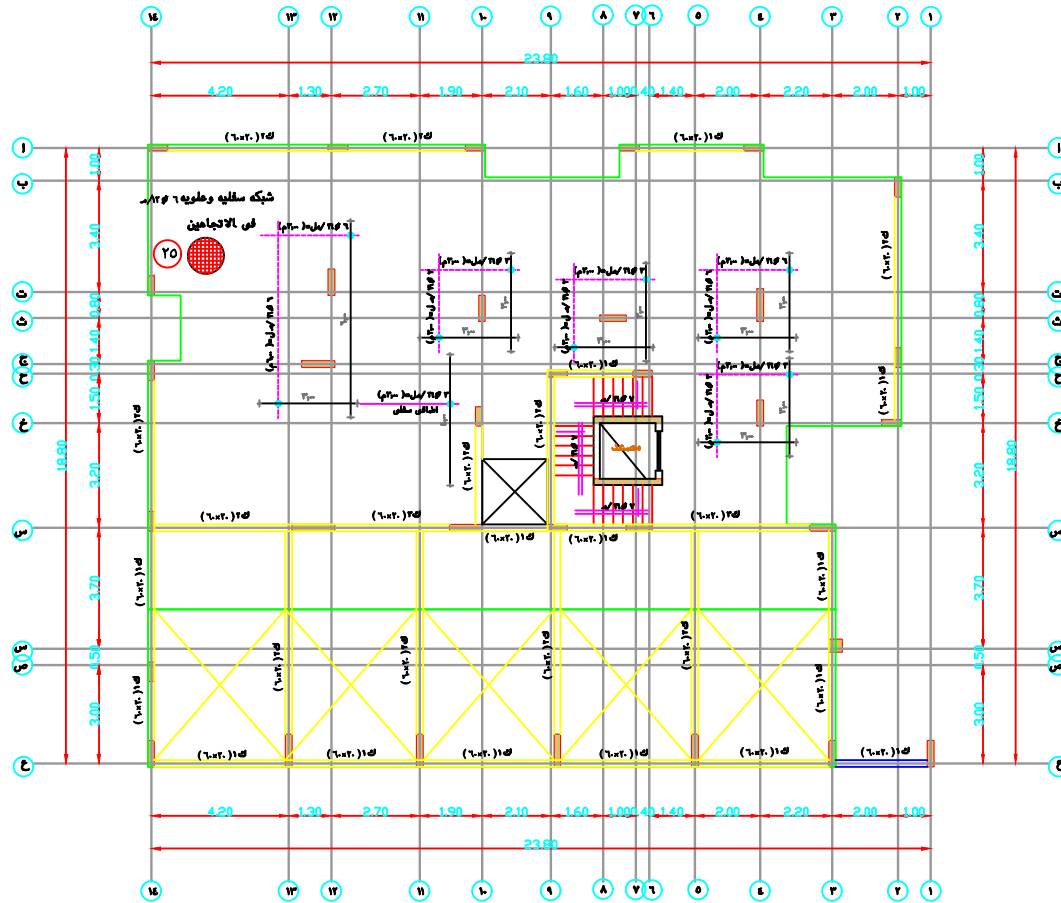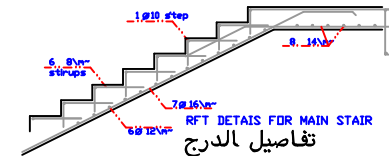

مكتب المهندس عمر بن سعيد بو سعيد
للاستشارات الهندسية
OMAR BOSAEED
CONSULTANT ENGINEER
تصميم عمارة تخطيط اشراف هندسي
رفع مساحي دراسة الاحمال الكهربائية

مكة المكرمة الشوكية
مبنى الانبار التجاري
مقابل محطة الشوكية للمحروقات
FAX-5335800 TEL-5335800
EMAIL-osboffice@hotmail.com

CLIENT : المالك

على عبدالله ال سليمة القرني

LOCATION : الموقع

مخطط ولي العهد رقم ٣

SUBJECT : الموضوع

انشاء عمارة سكنية

TITLE : عنوان اللوحة

سقف الدور الارضي

رقم اللوحة

04

SHEET NO

جدول نماذج تسليح الكمرات

النموذج	التسليح السفلي		التسليح العلوي	الكانات	ملاحظات
	مكسح	عدل			
ك ١	١٦ # ٣	---	١٢ # ٣	٨ # ٥ م	
ك ٢	١٦ # ٤	---	١٤ # ٣	٨ # ٥ م	
ك ٣	١٦ # ٦	---	١٦ # ٣	٨ # ٥ م	
ك ٤	١٦ # ٦	---	١٦ # ٦	٨ # ٥ م	٤ فروع
ك ٥	١٨ # ٢٥	١٦ # ٨	١٨ # ١٢	٨ # ٢ م	٤ فروع
ك ٦	١٦ # ١٨	---	١٦ # ٦	٨ # ٢ م	٤ فروع
ك ١	١٦ # ٣	---	١٦ # ٣	٨ # ٥ م	
ك ٢	١٦ # ٣	---	١٦ # ٦	٨ # ٥ م	

ملاحظات الاسقف

× اجهاد كسر المكعبات القياسية $10 \times 10 \times 10$ سم للخرسانة المسلحة المستخدمة في صب الاسقف ٣٠٠ كجم سم وذلك بعد ٢٨ يوم من صبها والخطة المقترحة هي ٨٠م^٢ ركام + ٤٠م^٢ بطحا + ٣٥٠ كجم اسمنت بورتلاند عادي ومحتوى المياه لا يتعدى ٤٥٪ من وزن الاسمنت يمتد حديد الكوابيل والشوك مرة ونصف طول البروز ويمتد الى الامام الحديد العلوي والمكسح و الحديد يستمر الى نهاية الكابولي

النوعى عن ٨٠٠ كج / م^٢



× ويمتد الحديد العلوي الى ١/٤ البحر المجاور الكمرات التي لا يوجد بها حديد مكسح يراعى مد تسليحها العلوي الى ١/٤ البحر المجاور

× يتم التكميخ بزاوية ٤٥ والكمرات التي يزيد عمقها عن ٧٠ سم على زاوية ٦٠

× كانات الاعمدة داخل الكمرات والبلاطات يجب معالجة الخرسانة بعد الصب وذلك برشها مرتين يوميا في غياب الشمس

× يجب مراجعة التفاصيل الانشائية قبل التنفيذ

× يجب مراجعة المحاور و الأبعاد مع اللوحات المعمارية قبل بدء التصميم الانشائي مسؤولية المكتب والتنفيذ مسؤولية المقاول

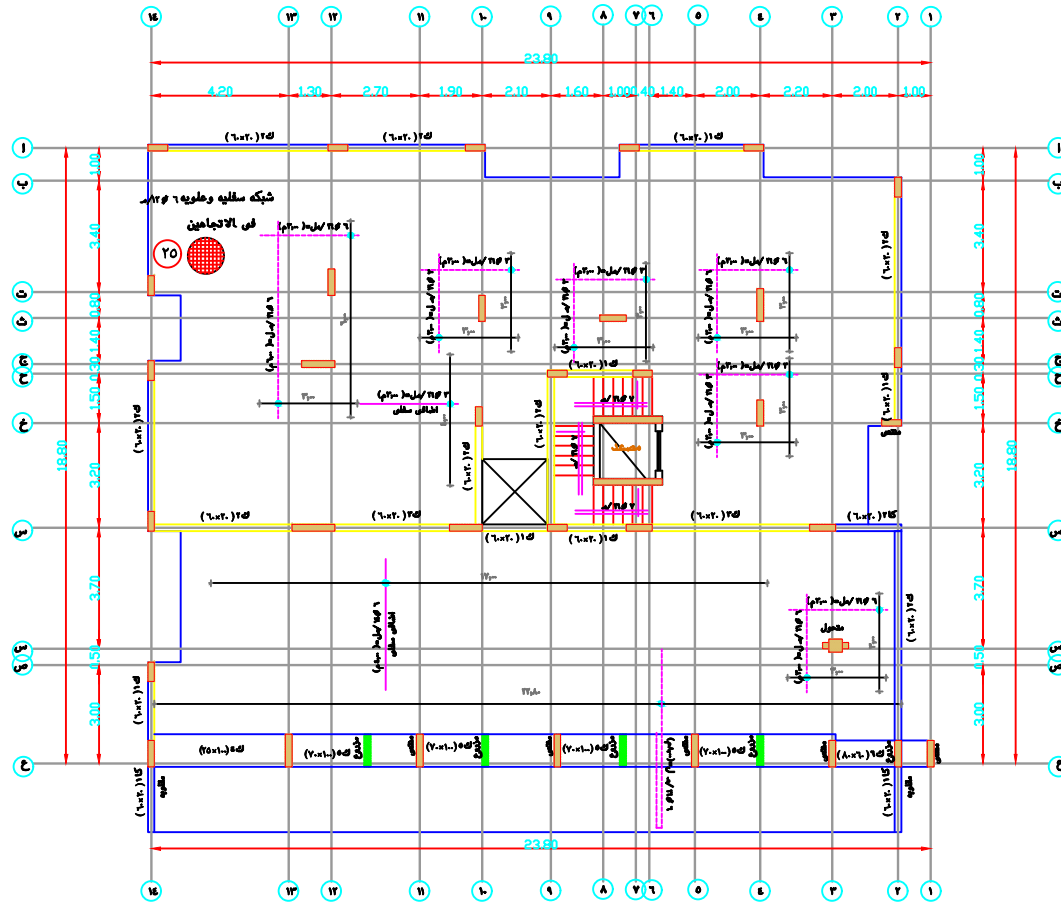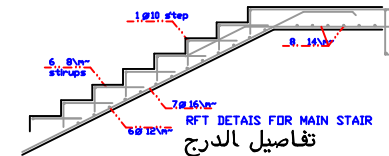

مكتب المهندس عمر بن سعيد بو سعيد
للاستشارات الهندسية
OMAR BOSAEED
CONSULTANT ENGINEER
تصميم عمارة تخطيط أشرف هندسي
رفع مساحي دراسة الاحمال الكهربائية

مكة المكرمة الشوكية
مبنى الانبار التجاري
مقابل محطة الشوكية للمحروقات
FAX-5335800 TEL-5335800
EMAIL-osboffice@hotmail.com

CLIENT : المالك

على عبدالله ال سليمة القرني

LOCATION : الموقع

مخطط ولي العهد رقم ٣

SUBJECT : الموضوع

انشاء عمارة سكنية


TITLE : عنوان اللوحة

سقف الدور الميزانين

رقم اللوحة

05

SHEET NO

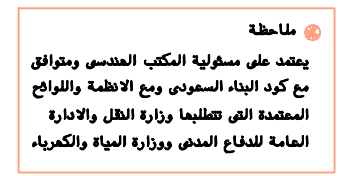

رقم اللوحة	الموضوع	المالك	CLIENT :
02	انشاء عمارة سكنية	علي عبدالله ال سليمانى القرنى	
SHEET NO	عنوان اللوحة	الوئع	LOCATION :
	مسقط افقى لدور الميزانين	مخطط ولى المعد رقم ٣	

تاريخ	DATE :	مقياس الرسم : SCALE :
٢٠٠٩		1 / 100

نوع اللوحة	٢٠٠٩
مبنى	٢٠٠٩
مخطط سلامة	٢٠٠٩
تخطيط مركزي	٢٠٠٩
تخطيط	٢٠٠٩

مكتب المهندس عمر بن سعيد بو سعيد
للاستشارات الهندسية
OMAR BOSEED
CONSULTANT ENGINEER
تصميم عمراني تخطيط اشراف هندسي
رفع مساحي دراسة الاحمال الكهربائية

مكة المكرمة الشوقية
مبنى الانبار التجارى
مقابل محطة الشوق للمحروقات
FAX-5335800 TEL-5335800
EMAIL-osboffice@hotmail.com

